147 MAJOR ST - SECTION A-A (REVISED, AS FOUND)
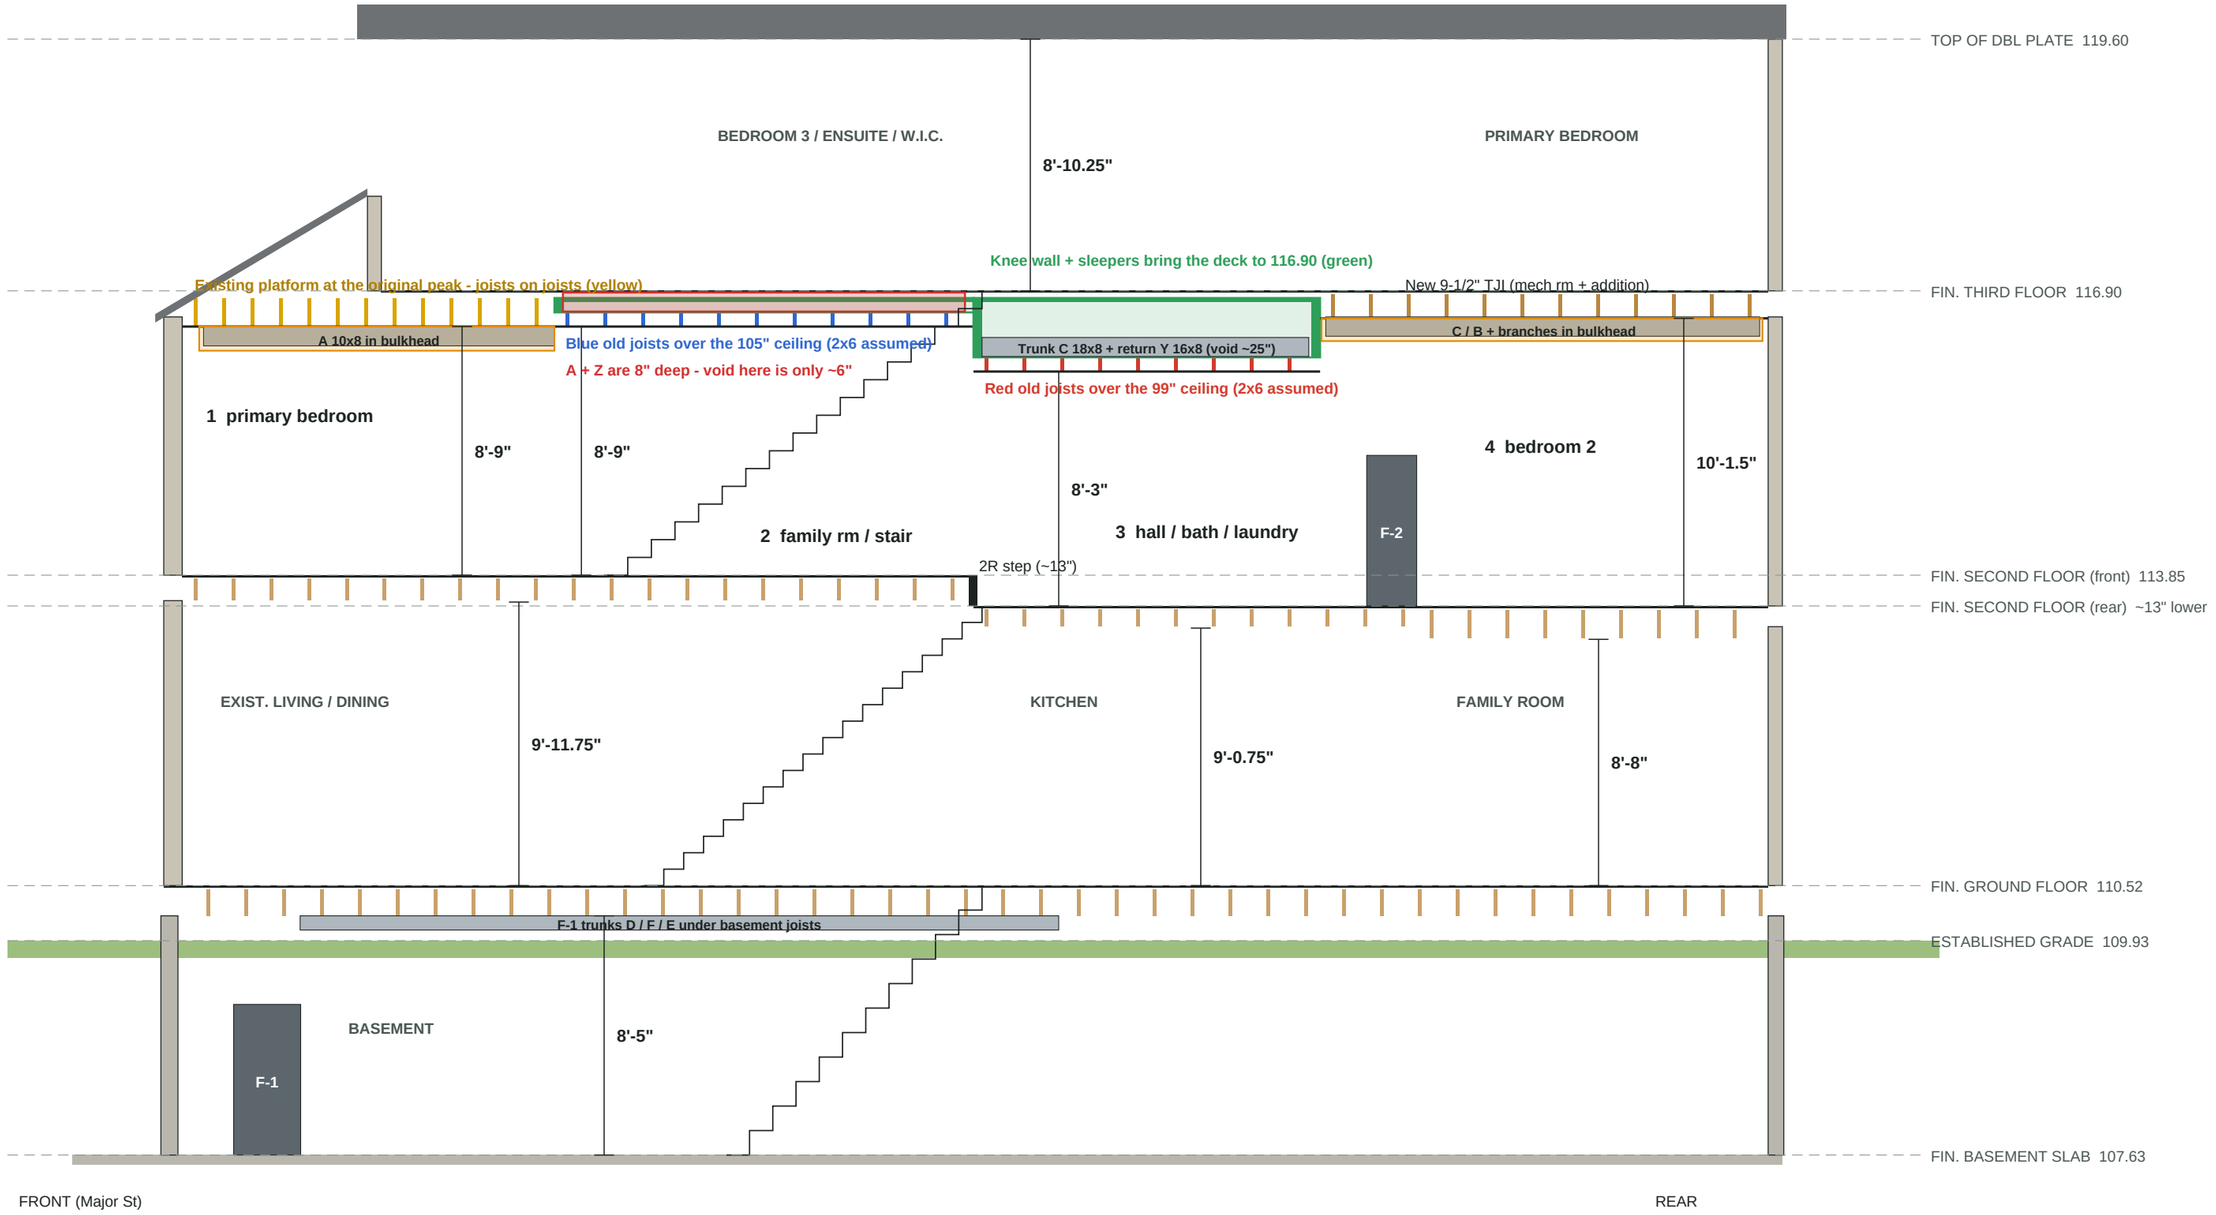
PalmView Custom Homes · coordination drawing · Oct 25, 2026 · NOT FOR CONSTRUCTION - for HVAC / framing coordination only
Permit A12 section + geodetic levels (A10-A12) + David site visit (framing and measured ceilings) + Raff sketch Oct 25 (platform, old joists, knee wall).
Assumed: old joists 2x6, 3rd-floor deck on 2x4 sleepers (3" build-up) at permit 116.90. Platform zone 1 front, blue 13'-3" to 28'-0", red 28'-0" to 40'-2" (mech room goes to 120"). Confirm on site.
Scale 3/16" = 1'-0" (11x17). Front (Major St) at left. Rear 2nd floor ~13" lower (fits David's 118" / 108" / 105" main-floor ceilings and UP 2R).